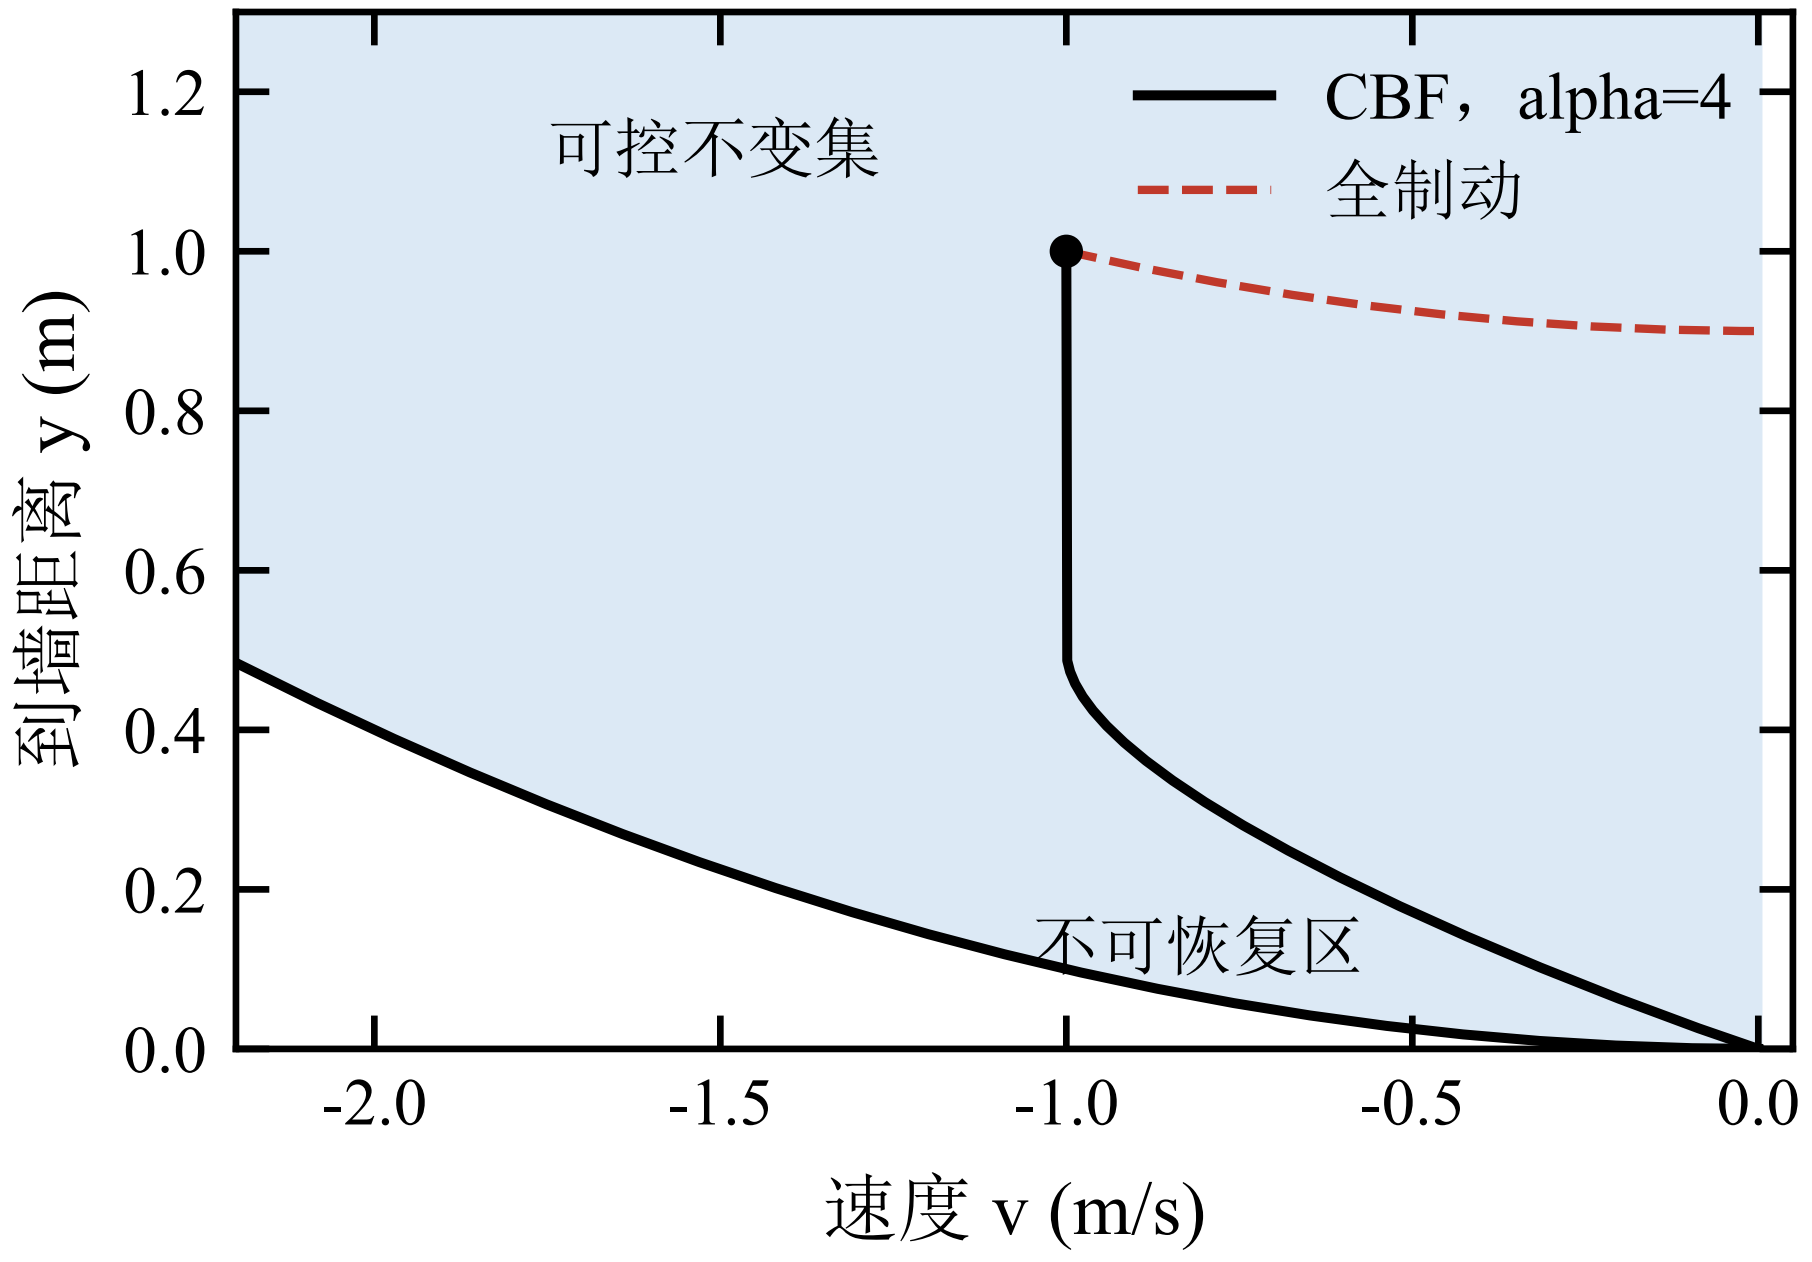
可控不变集
CBF，alpha=4
全制动
不可恢复区
到墙距离 y (m)
速度 v (m/s)
1.2
1.0
0.8
0.6
0.4
0.2
0.0
-2.0
-1.5
-1.0
-0.5
0.0